MAGDALENA HALBERG

ARQUITECTA

DOCUMENTACION TECNICA
&
VISUALIZACION ARQUITECTONICA



MAGDALENA HALBERG

ARQUITECTA

SOFTWARE

- AutoCAD
- SketchUp + V-Ray
- Lumion
- Adobe Photoshop
- Flujo de trabajo con IA

PERFIL PROFESIONAL

Desarrollo proyectos de arquitectura mediante documentación técnica, modelado 3D y visualización arquitectónica, generando soluciones coordinadas y construibles desde el desarrollo del diseño hasta la presentación final del proyecto.
Mi experiencia abarca proyectos residenciales, comerciales y desarrollos urbanos, participando en todas las etapas del proceso arquitectónico con un fuerte enfoque en la precisión, la claridad y la calidad de ejecución.

DOCUMENTACION TECNICA

Documentación ejecutiva precisa, coordinada y apta para construcción en proyectos residenciales, comerciales y corporativos.

MODELADO 3D

Modelos digitales precisos para comunicar la intención de diseño Y apoyar todas las etapas del desarrollo arquitectónico.

VISUALIZACION ARQUITECTONICA

Renders e imágenes de alta calidad que comunican el diseño, potencian presentaciones y acompañan procesos comerciales y de aprobación.

DESARROLLOS URBANOS

Masterplans, proyectos de subdivisión y documentación técnica para desarrollos urbanos e inmobiliarios de distintas escalas.

PROYECTO

01

VIVIENDA UNIFAMILIAR

Vivienda unifamiliar contemporánea diseñada para una empresa constructora privada, combinando una arquitectura moderna con espacios funcionales y eficientes.

ROL

Diseño de Anteproyecto
Documentación Técnica
Modelado 3D
Visualización

CLIENTE

Elemental Constructora

AÑO


2026

SOFTWARE


AutoCAD
SketchUp
Lumion + IA




PLANTA

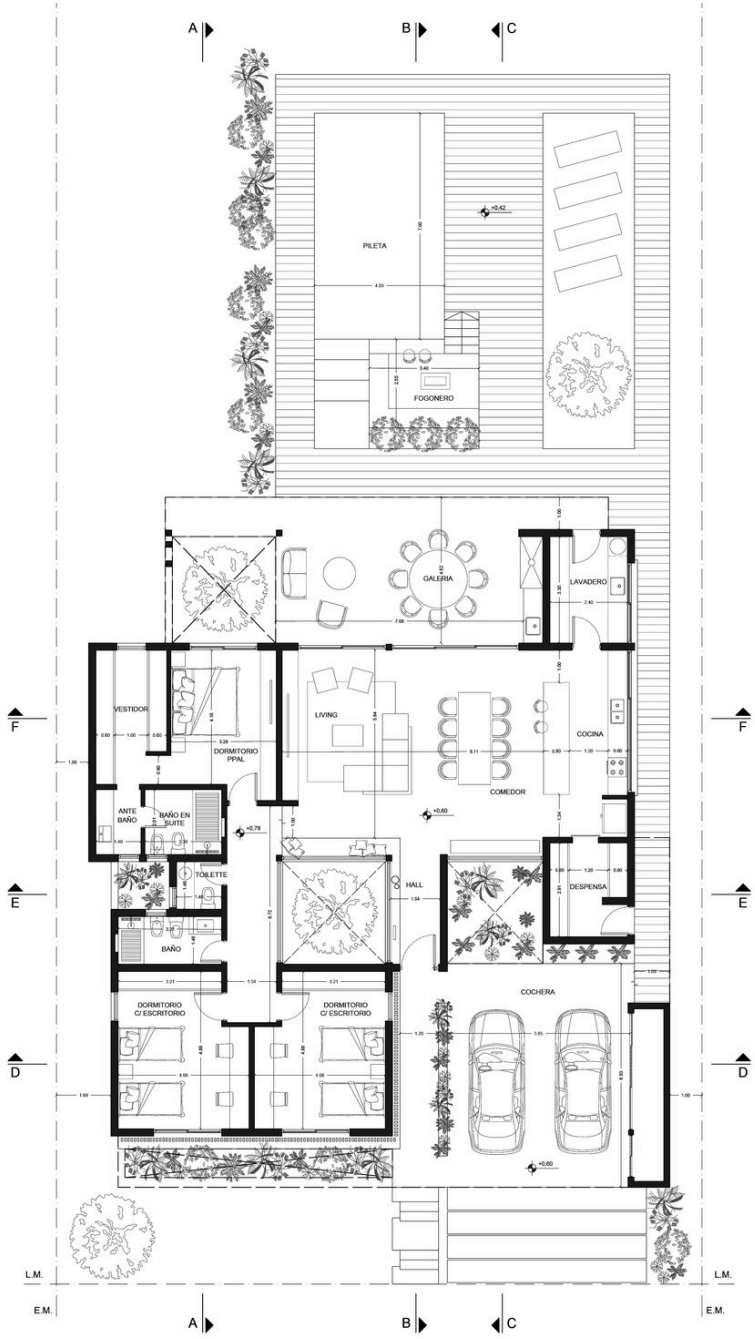


CORTE F-F

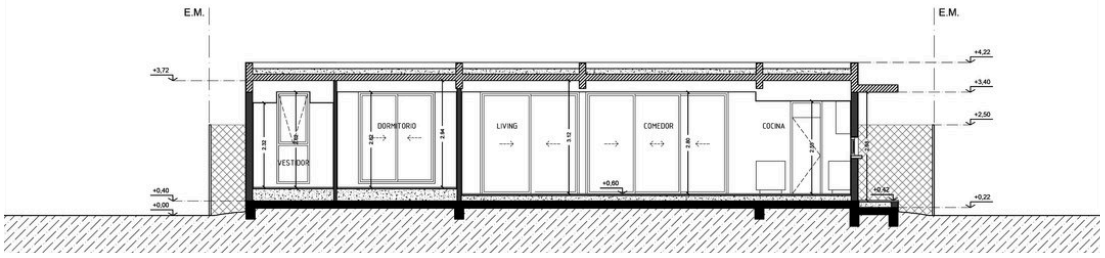


CORTE E-E

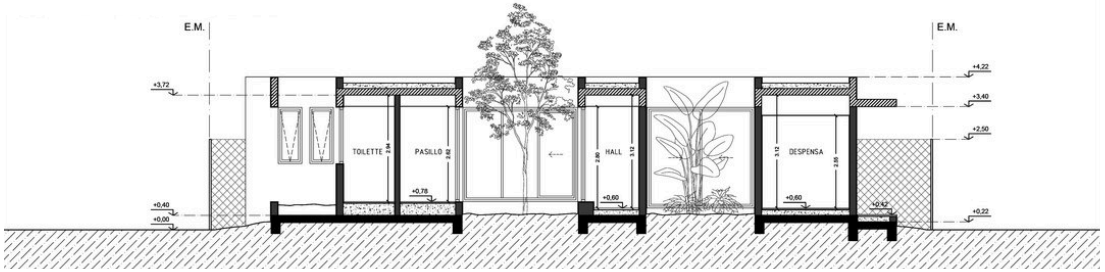


CORTE D-D

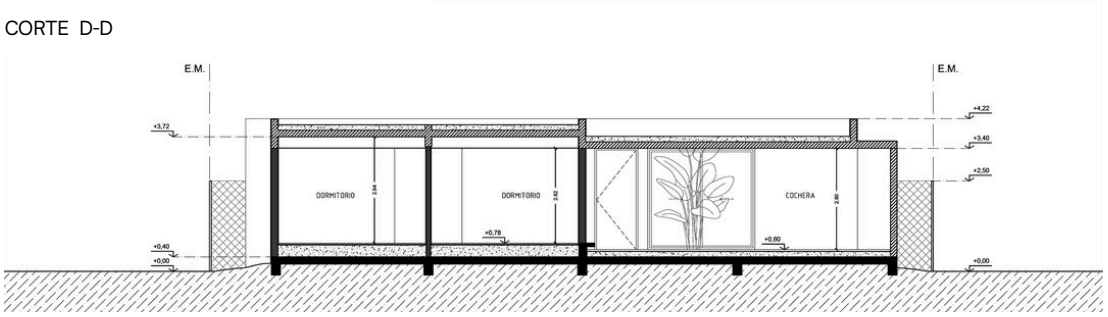

PLANTA DE FUNDACIONES

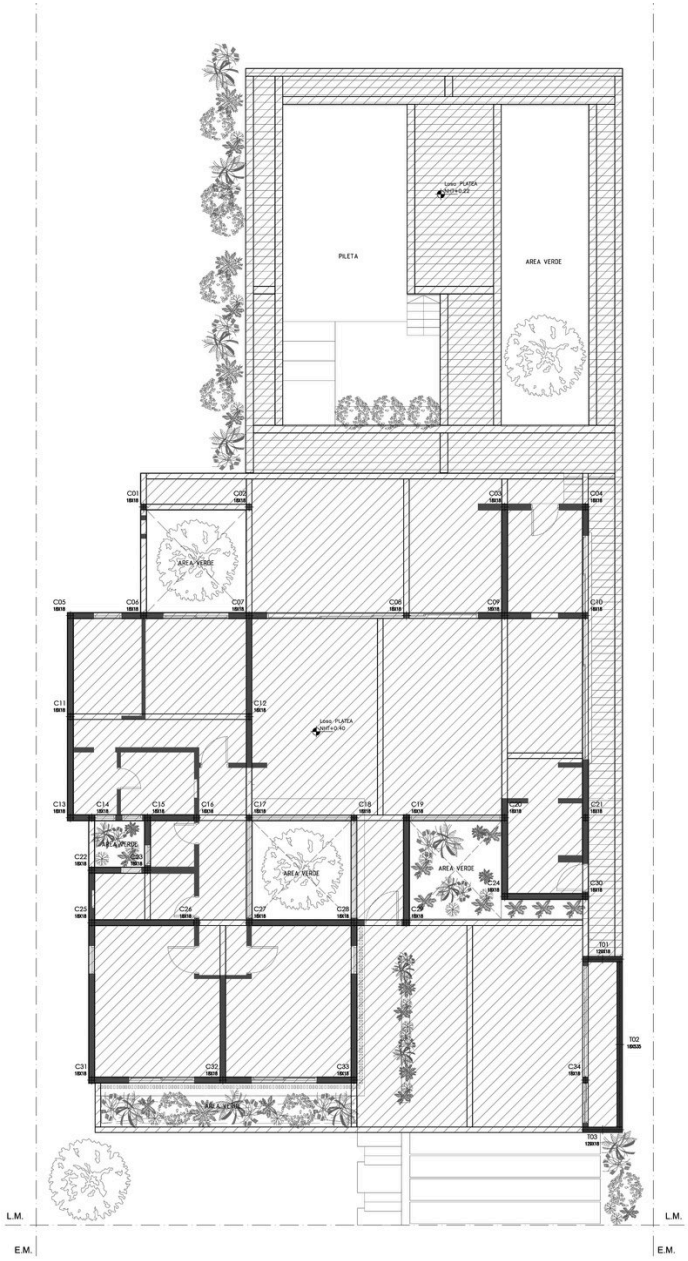

ESTRUCTURA SOBRE P.B.

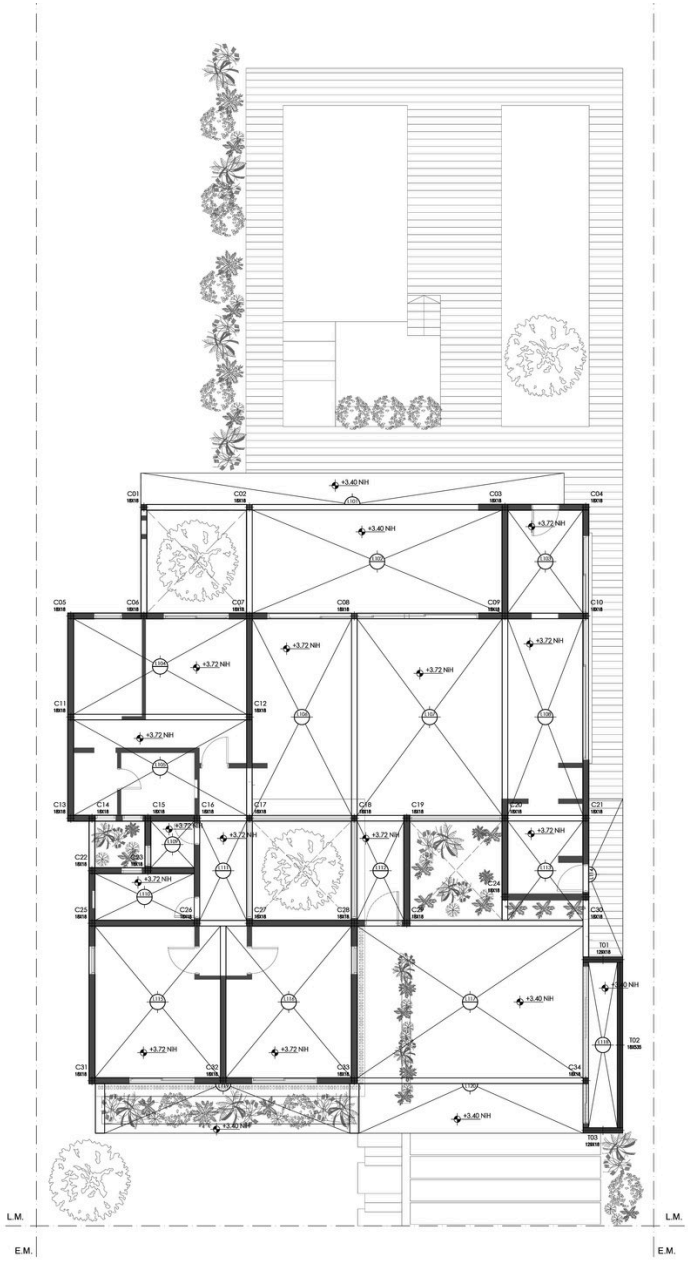

01 VISUALIZACION













PROYECTO

02

VIVIENDA UNIFAMILIAR

Vivienda unifamiliar contemporánea concebida para potenciar la iluminación natural, los espacios abiertos y la relación entre el interior y el exterior.

ROL

Diseño de Anteproyecto
Documentación Técnica
Modelado 3D
Visualización

CLIENTE

Elemental Constructora

AÑO


2026

SOFTWARE


AutoCAD
SketchUp
Lumion + IA




PLANTA BAJA

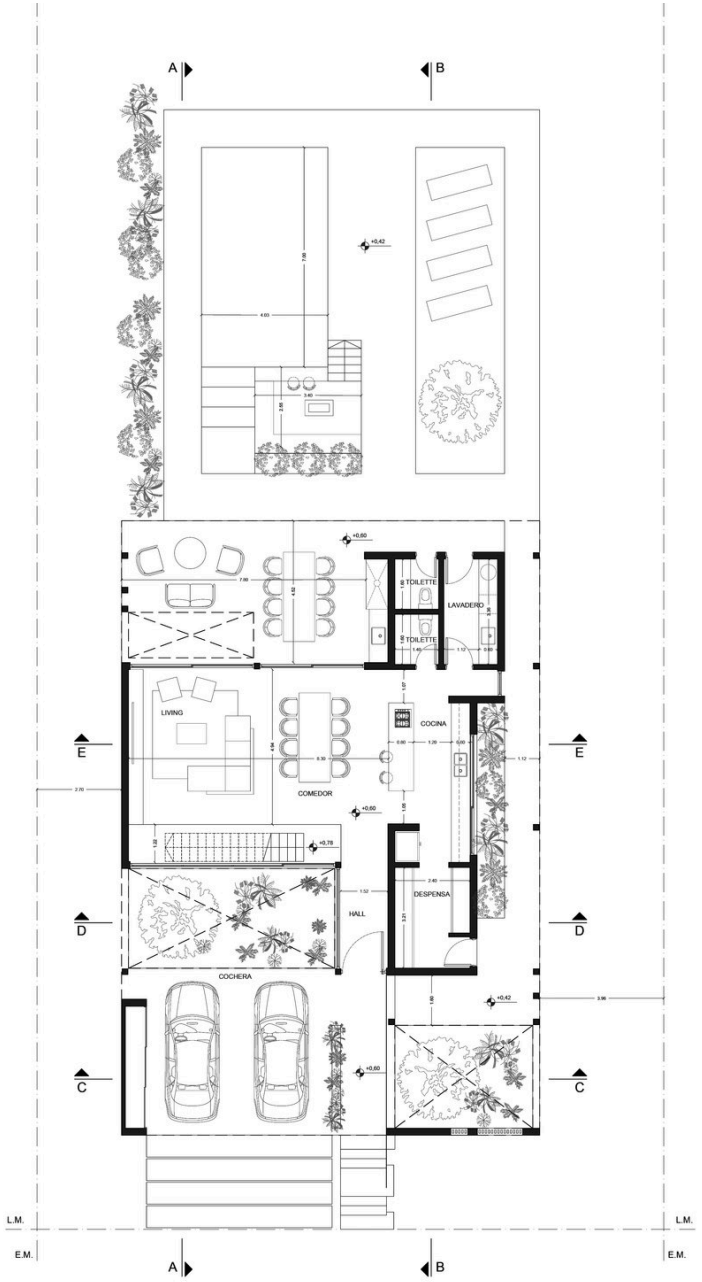


CORTE C-C

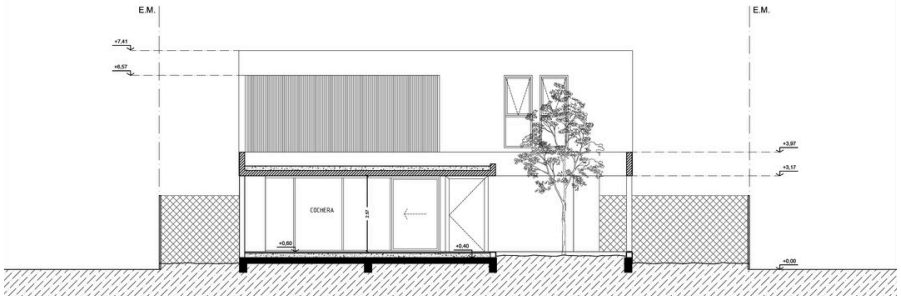


CORTE D-D

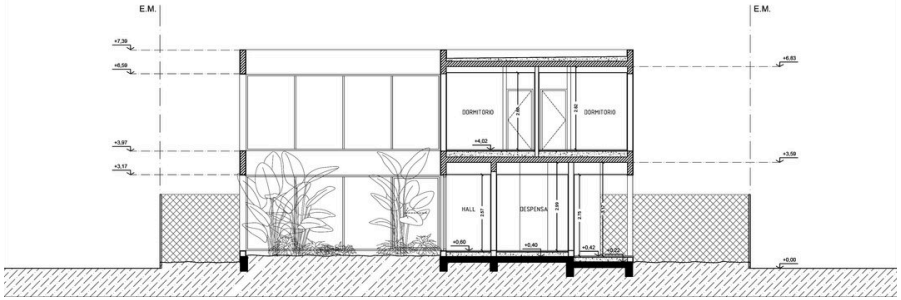


CORTE A-A

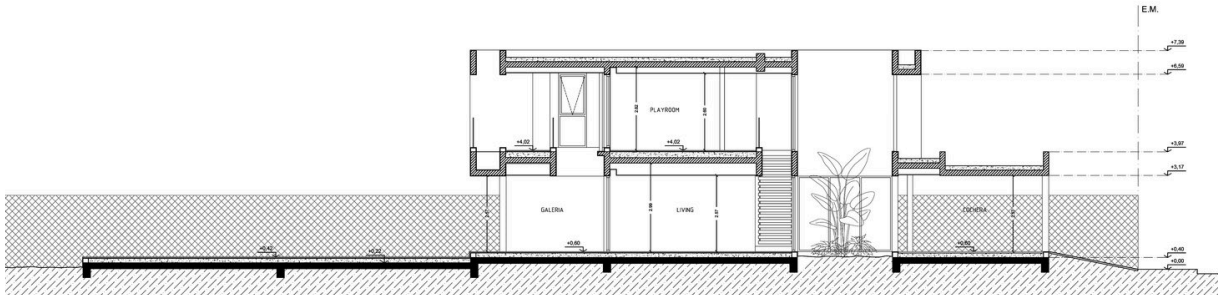


DESGÜE CLOACAL (PLANTA BAJA)

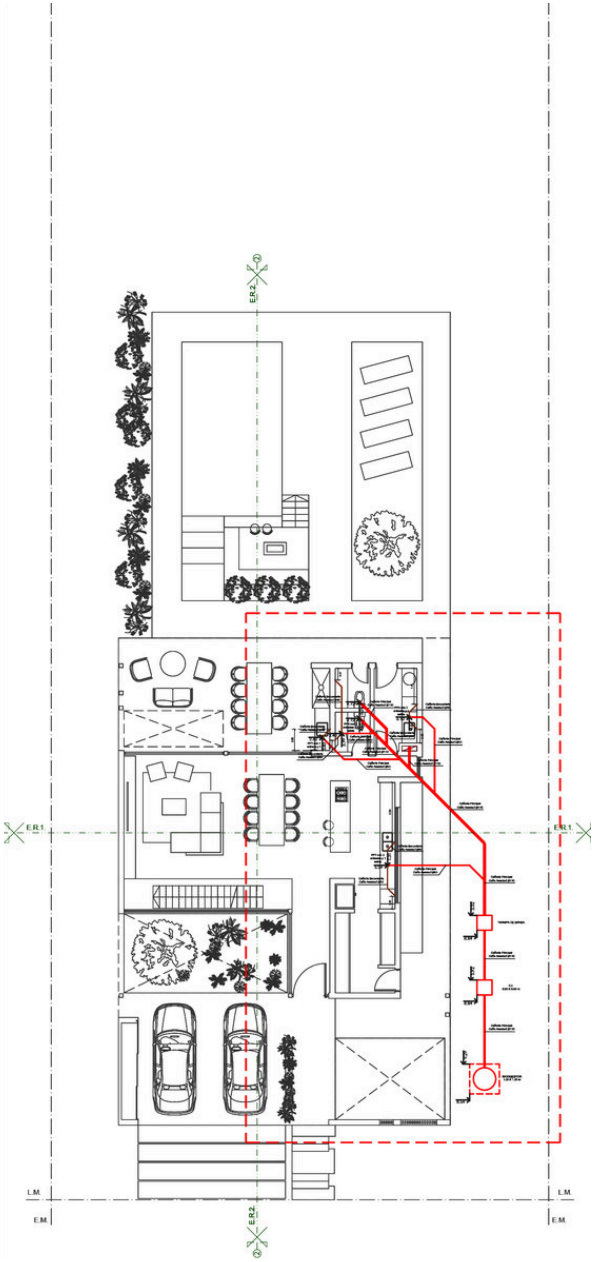


DESAGÜE CLOACAL (ZOOM PLANTA BAJA)

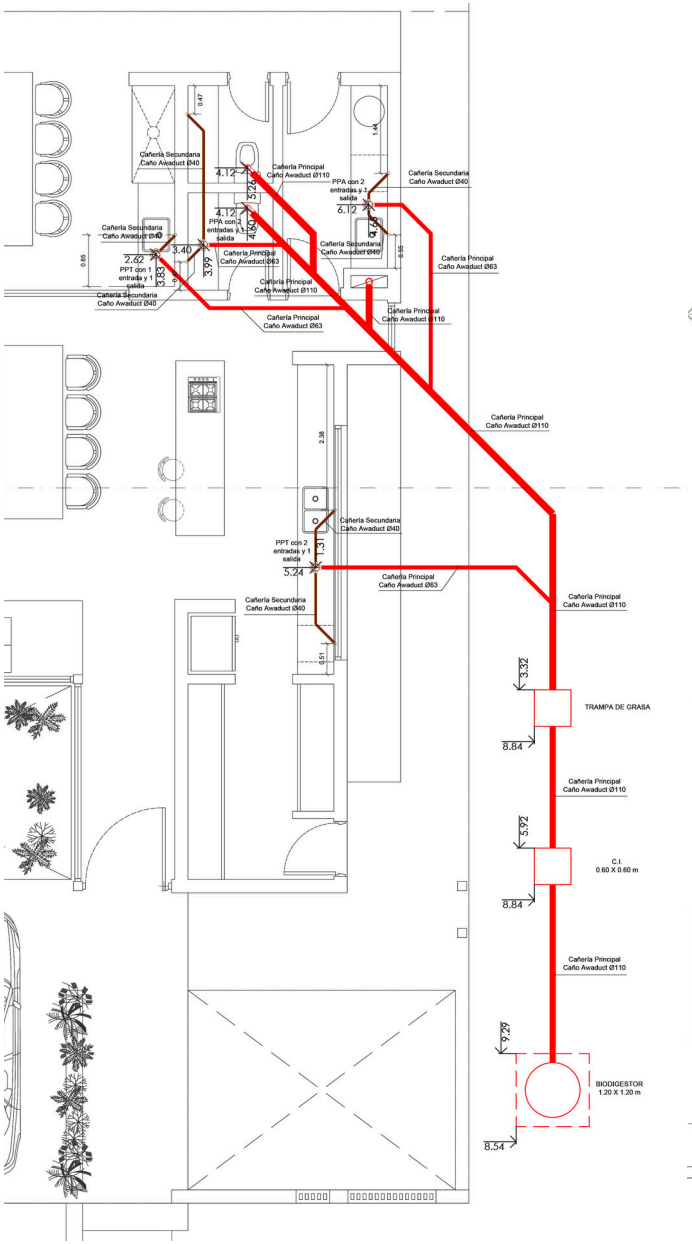

DESAGÜE CLOACAL (PRIMER PISO)

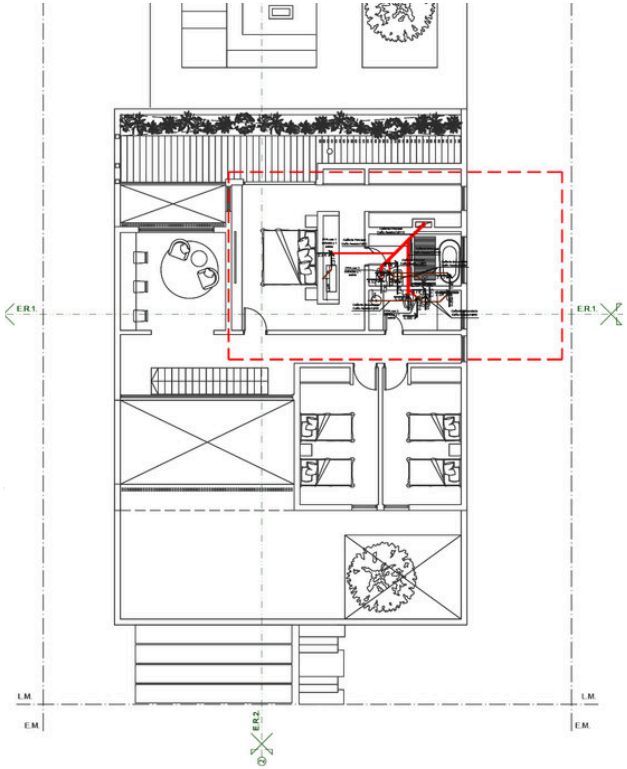

DESAGÜE CLOACAL (ZOOM PRIMER PISO)

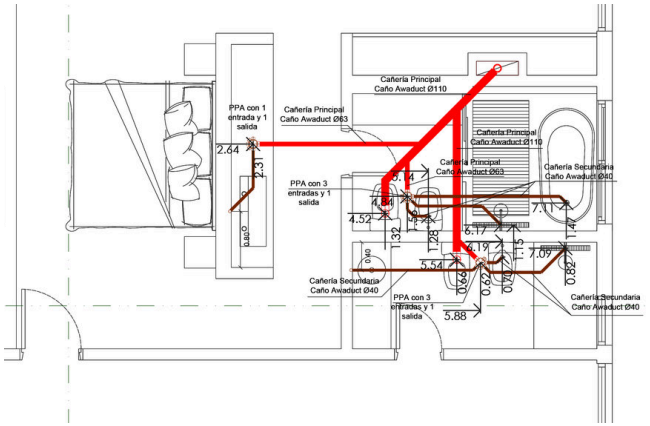













PROYECTO

03

VIVIENDA UNIFAMILIAR

Vivienda unifamiliar contemporánea diseñada con una distribución funcional, espacios luminosos y una fuerte integración con el paisaje.

ROL

Diseño de Anteproyecto
Modelado 3D
Visualización

CLIENTE

Cliente Particular

AÑO


2026

SOFTWARE


AutoCAD
SketchUp
Flujo de trabajo con IA




PLANTA

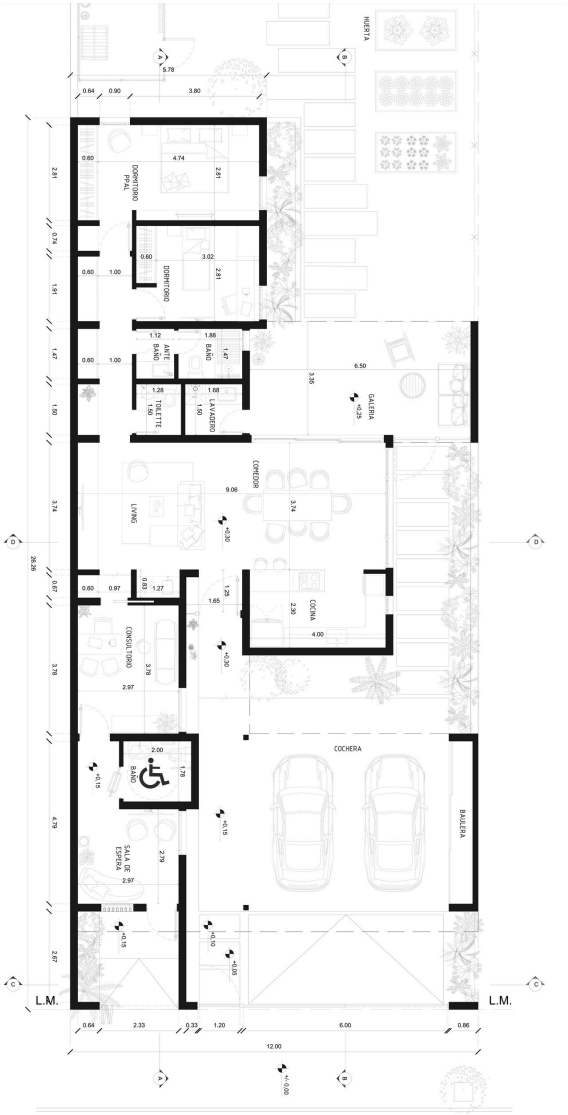


CORTE A-A

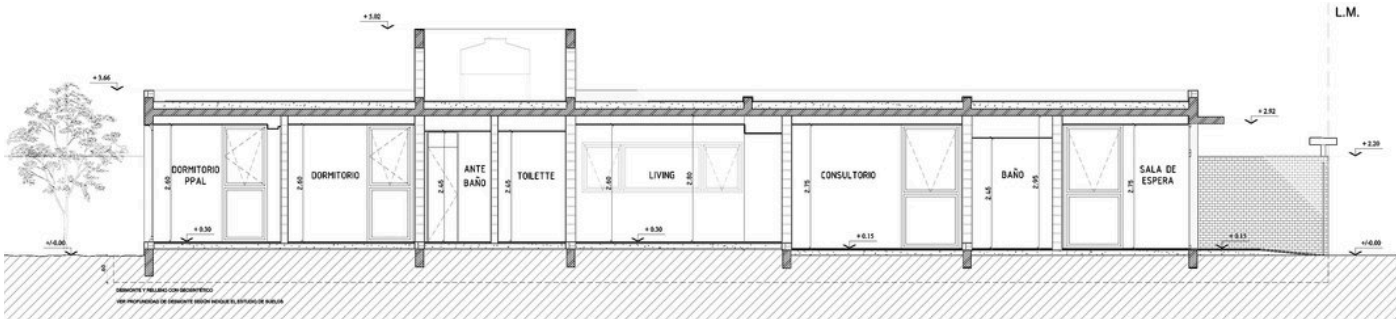


CORTE B-B

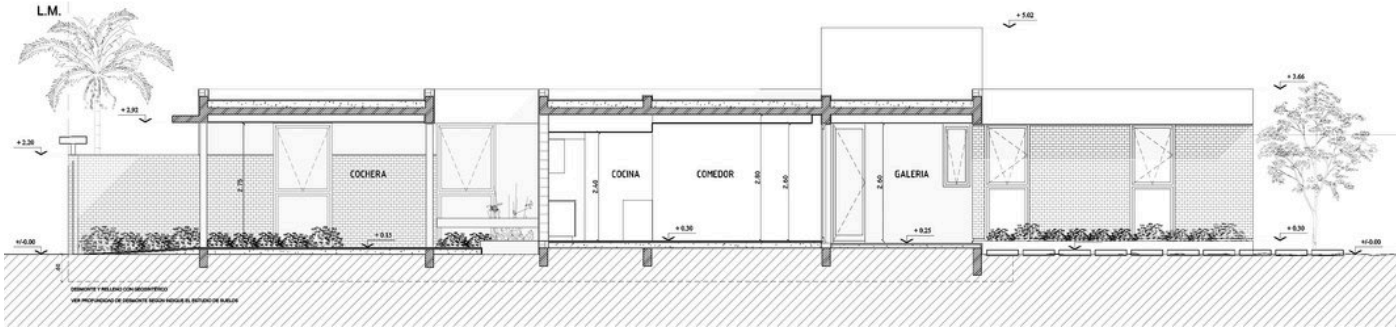

CORTE D-D

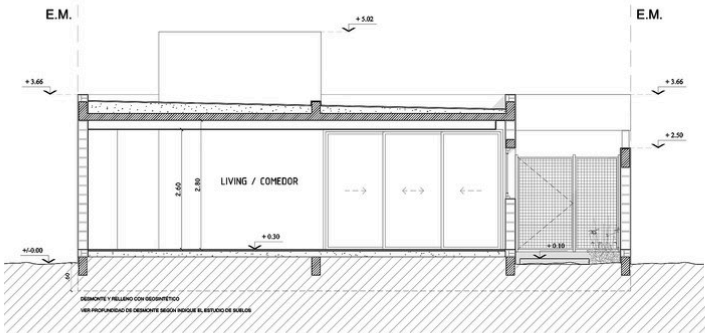

VISTA FRENTE

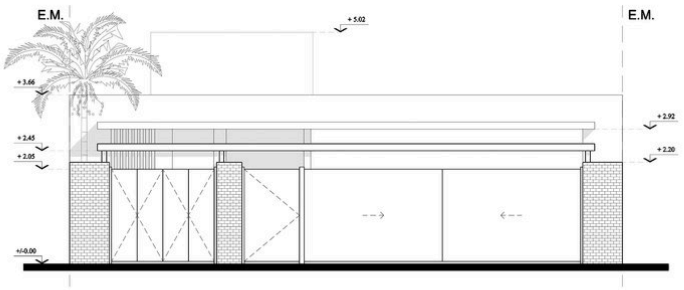

03 VISUALIZACION

















PROYECTO

04

REMODELACION DE OFICINA

Remodelación integral de oficinas corporativas orientada a mejorar la funcionalidad, la colaboración y la experiencia de los espacios de trabajo.

ROL

Diseño de Anteproyecto
Documentación Técnica
Modelado 3D
Visualización

CLIENTE

Elemental Constructora

AÑO

2026

SOFTWARE


AutoCAD

SketchUp


Flujo de trabajo con IA




PLANTA

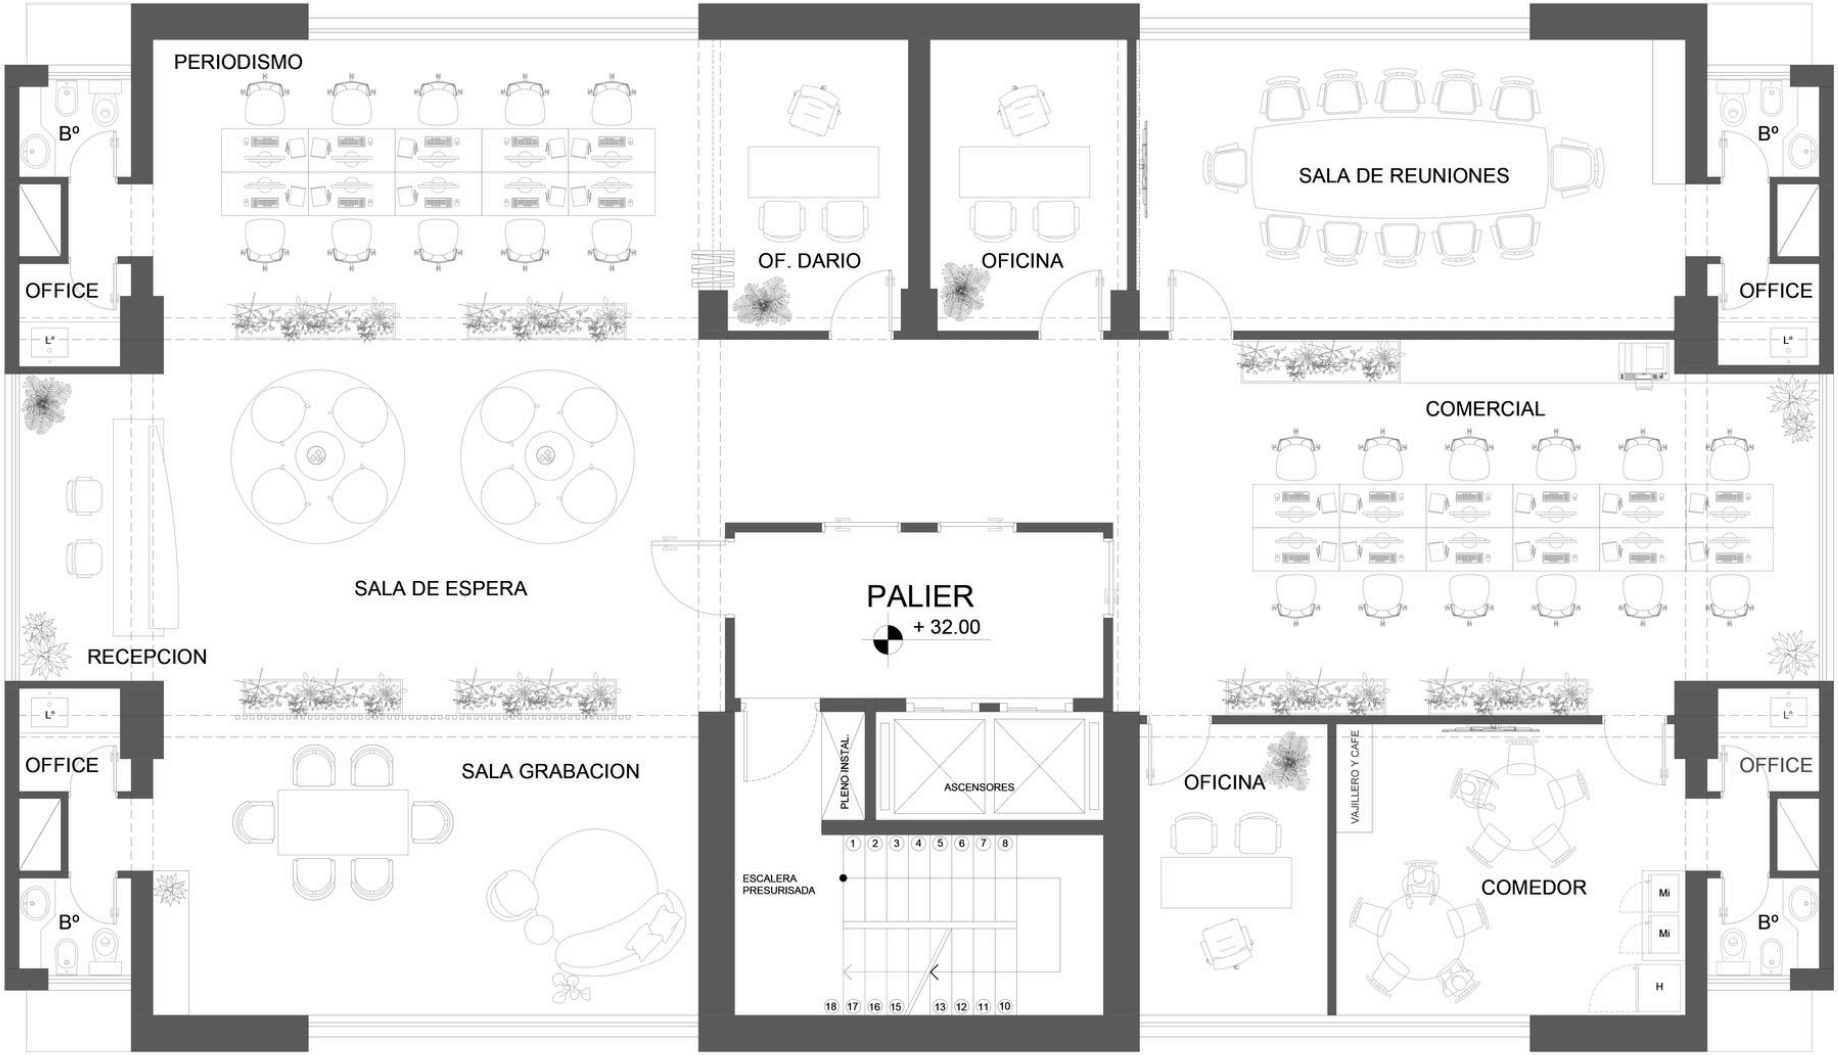
PERIODISMO
Bº
OFFICE
OF. DARIO
OFICINA
SALA DE REUNIONES
Bº
OFFICE
COMERCIAL
SALA DE ESPERA
PALIER
+ 32.00
RECEPCION
OFFICE
SALA GRABACION
PLENO INSTAL.
ASCENSORES
OFICINA
VAJILLERO Y CAFE
OFFICE
ESCALERA PRESURISADA
COMEDOR
Bº
Bº

REPLANTEO MUROS

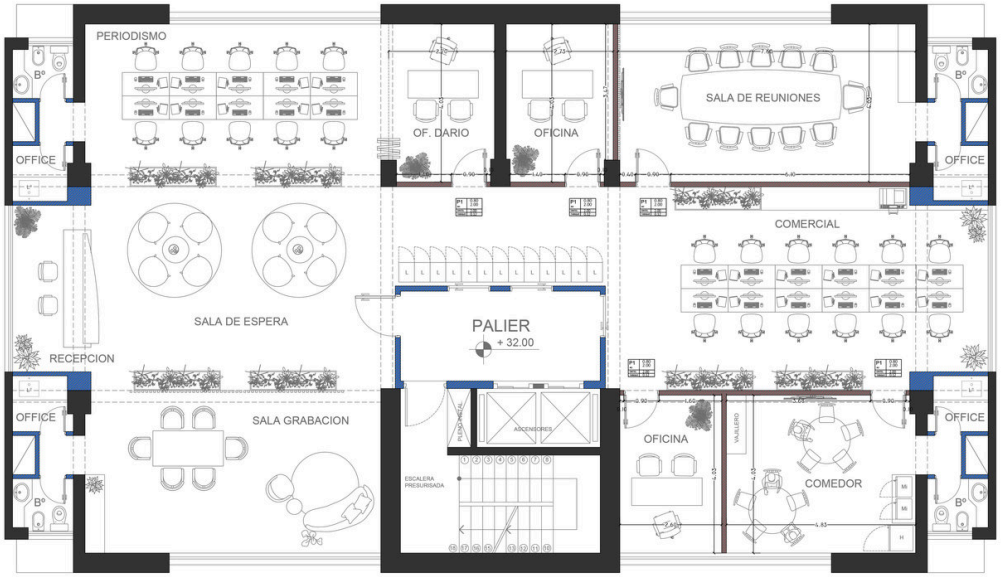


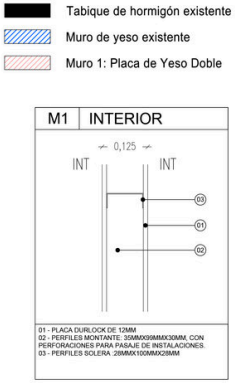


PLANILLA DE MUEBLES



ELECTRICIDAD

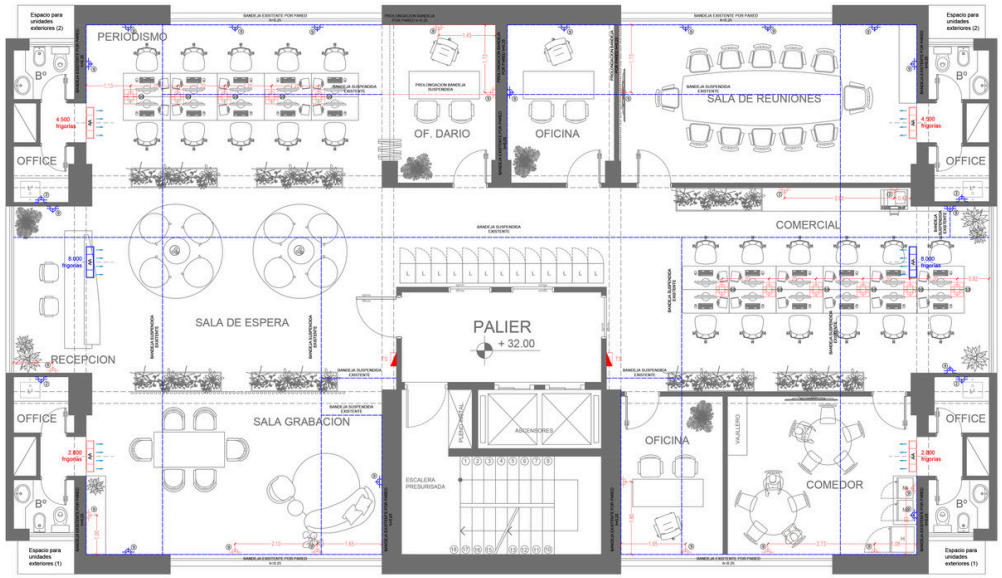



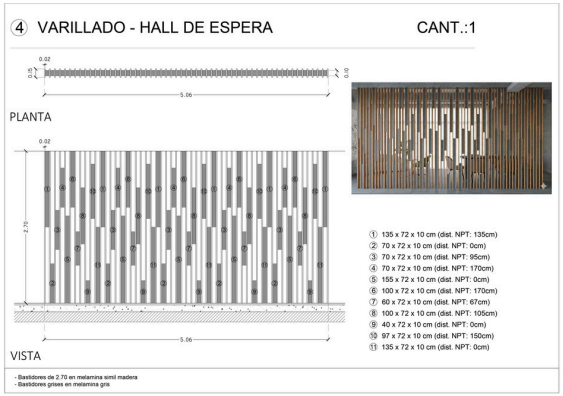




DELSUD







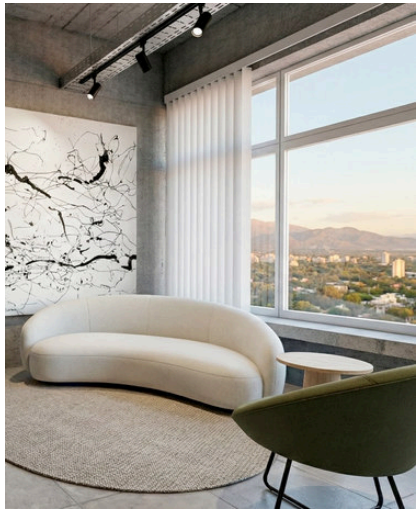

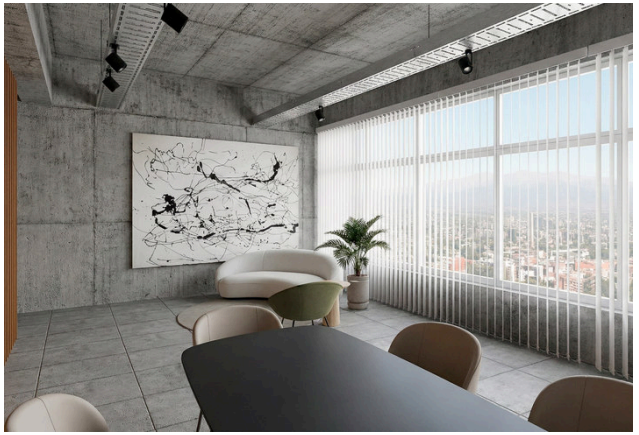

PROYECTO

05

REMODELACION DE RESTAURANTE

Reconversión de una vivienda histórica en un restaurante contemporáneo, preservando el carácter arquitectónico original e incorporando nuevos usos y espacios gastronómicos.

ROL

Diseño de Anteproyecto
Documentación Técnica
Modelado 3D
Visualización

CLIENTE

Elemental Constructora

AÑO


2026

SOFTWARE

- AutoCAD
- SketchUp
- Flujo de trabajo con IA



PLANTA BAJA

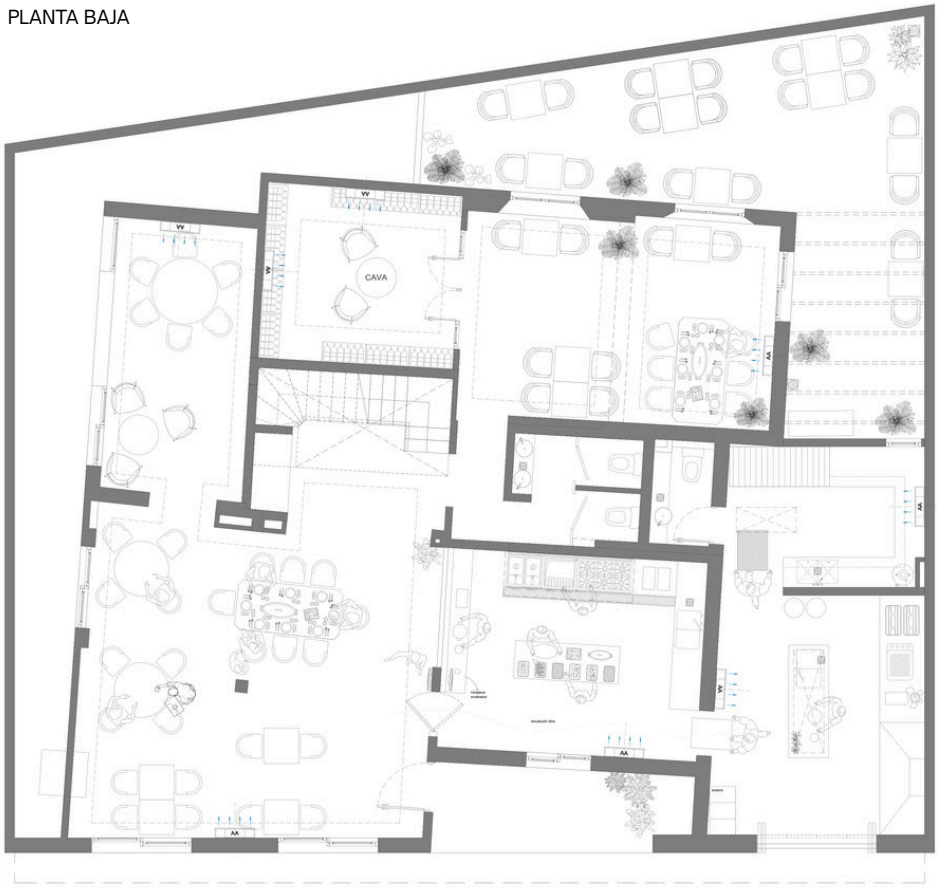

PRIMER PISO



PLANO DE DEMOLICION



REFERENCIAS


- A DEMOLER MUROS Y ABERTURAS
- A DEMOLER MESADAS
- A DEMOLER SEMICUBIERTO

Artefactos a retirar:

5. RADIADOR
6. ESTUFA
7. RADIADOR
8. RADIADOR
9. TANQUE CISTERNA, CALDERA, TANQUE ELEVADO


PLANILLA DE MUEBLES


L MUEBLE SALÓN 3 - PA

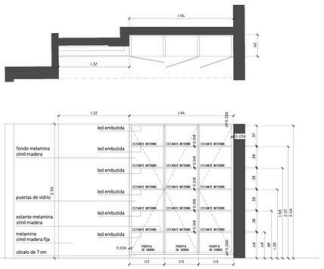



ELECTRICAL PLANS

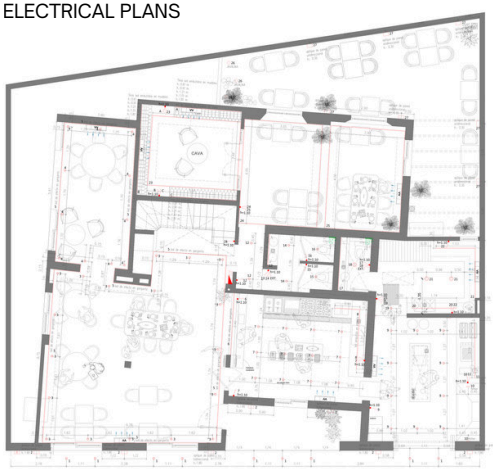

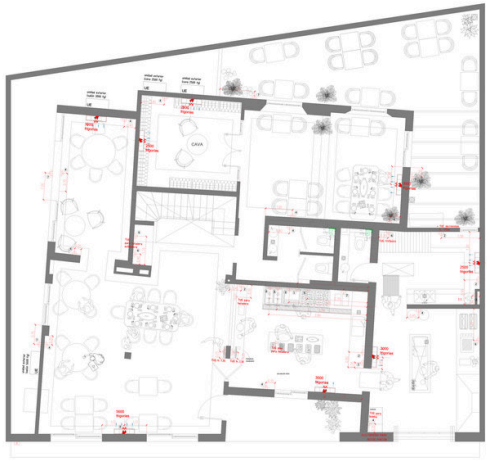


PLANILLA DE MESADAS

4 MESADA COCINA - PLANTA BAJA




TIPO DE MESADA: granito negro
ESPESOR: 2 cm
TRAFORO: no
BACHA: no
GRIFERÍA: no
ZÓCALO: 8 cm
FRENTIN: no
OBSERVACIONES: lleva ménsulas - revisar detalles en obra

5 ISLA PARRILLA - PLANTA BAJA

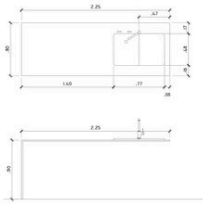

TIPO DE MESADA: granito negro
ESPESOR: 2 cm
TRAFORO: 1
BACHA: 1 de embutir
GRIFERÍA: 1
ZÓCALO: no
FRENTIN: no
OBSERVACIONES: apoya sobre mueble - revisar detalles en obra


9 MESADA COCINA - PLANTA BAJA

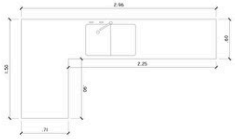

Espacio para mesada de acero inoxidable con bacha doble incorporada.

OBSERVACIONES: revisar detalles en obra

10 MESADA ZONA DE LAVADO - PLANTA BAJA

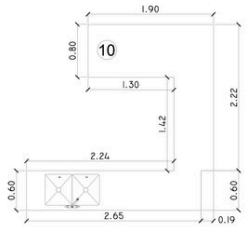

Espacio para mesada de acero inoxidable con bacha doble incorporada.


OBSERVACIONES: revisar detalles en obra









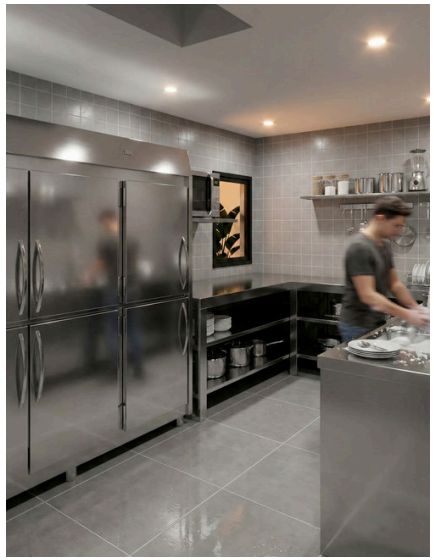



PROYECTO

06

DESARROLLO RESIDENCIAL

Masterplan para un desarrollo residencial con espacios comunes, áreas recreativas y una propuesta urbana integrada.

ROL

Documentación Técnica
Modelado 3D
Visualización

CLIENTE

Desarrollos Delsud

AÑO

2024

SOFTWARE


AutoCAD
SketchUp + Vray
Photoshop





N
NE
E
S
O

PLANO MUNICIPAL CLUB HOUSE


CLUB HOUSE

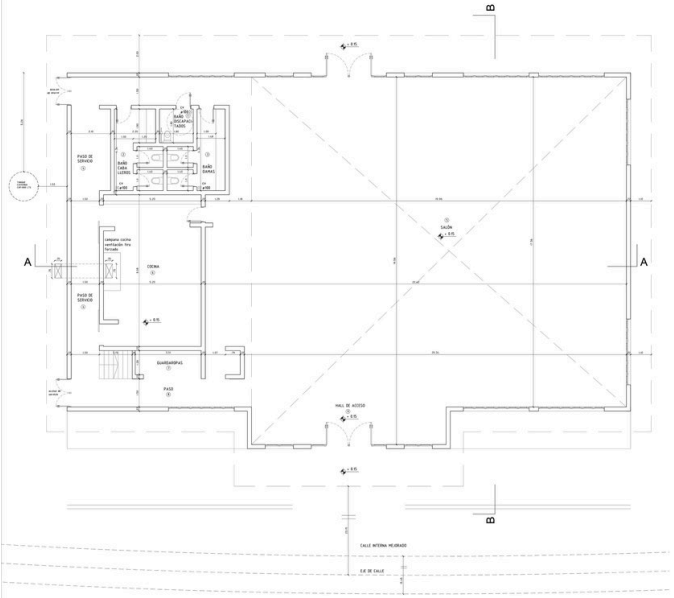

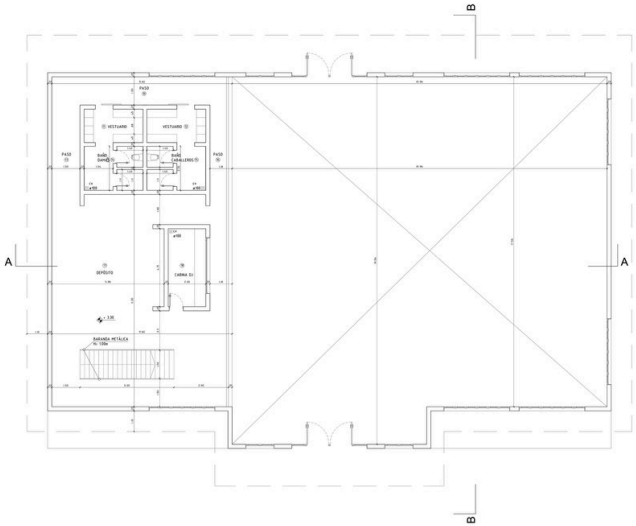


PLANTA BAJA ESC. 1:100


PLANTA ALTA ESC. 1:100

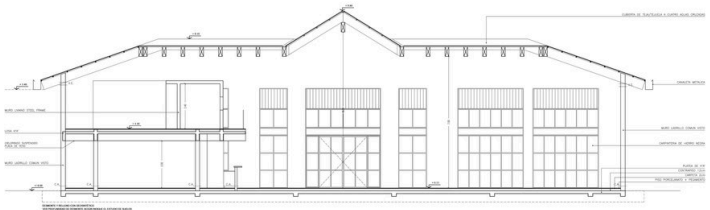


CORTE A-A ESC. 1:100

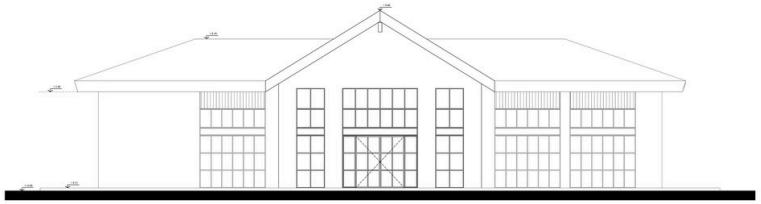

VISTA NORESTE ESC. 1:100

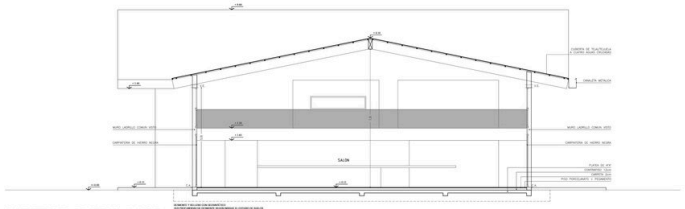

CORTE B-B ESC. 1:100

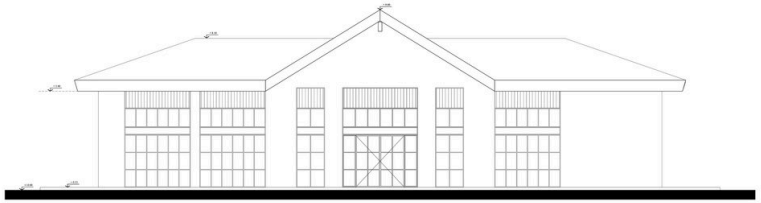


VISTA NORSTE ESC. 1:100

NOTA DE SERVICIOS


	SI	NO
AGUA CORRIENTE		X
CLOACAS		X
PAVIMENTO		X
GAS NATURAL		X
ELECTRICIDAD	X	

PLANO GENERAL UBICACION
ESC. 1:1500

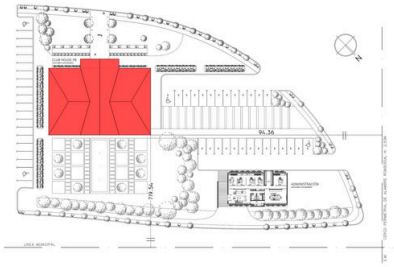

SILUETA DE SUPERFICIES
ESC. 1:200

PLANTA BAJA

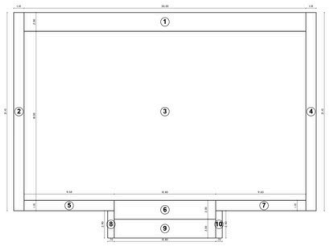

PLANTA ALTA



BALANCE DE SUPERFICIES

	S. CUBIERTA		S. SEMICUBIERTA	
	N°	m2	m2	N°
PB	1			60.00
	2			23.21
	3	540.00		
	4			23.21
	5			10.54
	6	21.60		
	7			10.56
	8			2.03
	9			21.60
	10			2.03
PA	11	169.26		
T		730.86	T	153.18
T		884.04		

REFERENCIAS
A CONSTRUIR
EXISTENTE

PLANO DE ANTEPROYECTO URBANISTICO

NOMBRE DEL EMPRENDIMIENTO: MIRAZUR

DESTINO:CLUB DE CAMPO
PARTIDO: MAGDALENA
LOCALIDAD: MAGDALENA

PROPIETARIOS: BASVIL S.A.S y GRAVA MOVIMIENTOS DE SUELOS Y VENTA DE MATERIALES S.R.L.

NOMENCLATURA CATASTRAL
Circ.: VI Secc: Ch. Qta. Fr. Mz. Parc. 2019 y 2020

ORDENANZA N°	32/83	BALANCE DE SUPERFICIE	
DECRETO LEY 8912/77- DECRETOS 9404/86 y 27/98		Sup. total de la fracción:	50,00 Has.
ZONA AREA RURAL		Sup. ½ calles a ceder:	Has.
INDICADORES URBANISTICOS DE LA ZONA		Sup. NETA del emprendimiento:	49,87 Has. 100 %
Dimensión mínima de parcela:	FOS:	Sup. residenciales:	24,70 Has. 49,52 %
FRENTE(m): 20	FOT:	Sup. circulacion:	14,25 Has. 28,59 %
SUPERFICIE (m2): 600	DENSIDAD:	Sup. espacios comunes:	10,92 Has. 21,89 %
INDICADORES URBANISTICOS DE PROYECTO		CANTIDAD DE LOTES: 350	
FOS: 0,3	(Densidad de proyecto/hab.ha.)	CANTIDAD TOTAL DE VIVIENDAS: 350	
FOT: 0,5	NETA 565 hab/Ha	N° de viviendas unifamiliares: 350	
	BRUTA 280 hab/Ha	N° de viviendas multifamiliares	

PROFESIONALES	PROPIETARIOS	
Título: Arquitecta	Apellidos: Vila Basualdo	Apellidos: Lima
Apellidos: Botta	Nombres: Francisco Alberto	Nombres: Nadia Antonella
Nombres: María José	Caracter: Administrador Titular (Basvil S.A.S.)	Caracter: Apoderada (Grava movimientos de suelos y venta de materiales S.R.L.)
Domicilio: Calle 137 N° 2749 Hernandez - La Plata	Domicilio: 37 N° 125 La Plata	Domicilio: 519 N° 6348 La Plata
Firma	Firma	Firma

RESTRICCIONES

- Las restricciones deberán constar en las escrituras traslativas
- En la zona del electroducto no se permitirán construcciones de ningún tipo ni árboles.
- En el área adyacente a la zona del electroducto no podrán erigirse instalaciones o efectuar plantaciones de especies que en su caída puedan ocasionar daños al electroducto



















PROYECTO

07

MASTERPLAN COSTERO

Masterplan para una comunidad residencial de uso mixto que integra barrios residenciales, espacios recreativos, áreas comerciales y equipamientos turísticos en un entorno costero.

ROL

Documentación Técnica
Modelado 3D
Visualización

CLIENTE

Desarrollos Delsud

AÑO


2026

SOFTWARE

AutoCAD
SketchUp
Flujo de trabajo con IA



- LOTES RESIDENCIALES
- AMENITIES Y DEPORTES
- PASEO COMERCIAL
- CLUB DE PLAYA
- AREAS VERDES
- CIRCULACION

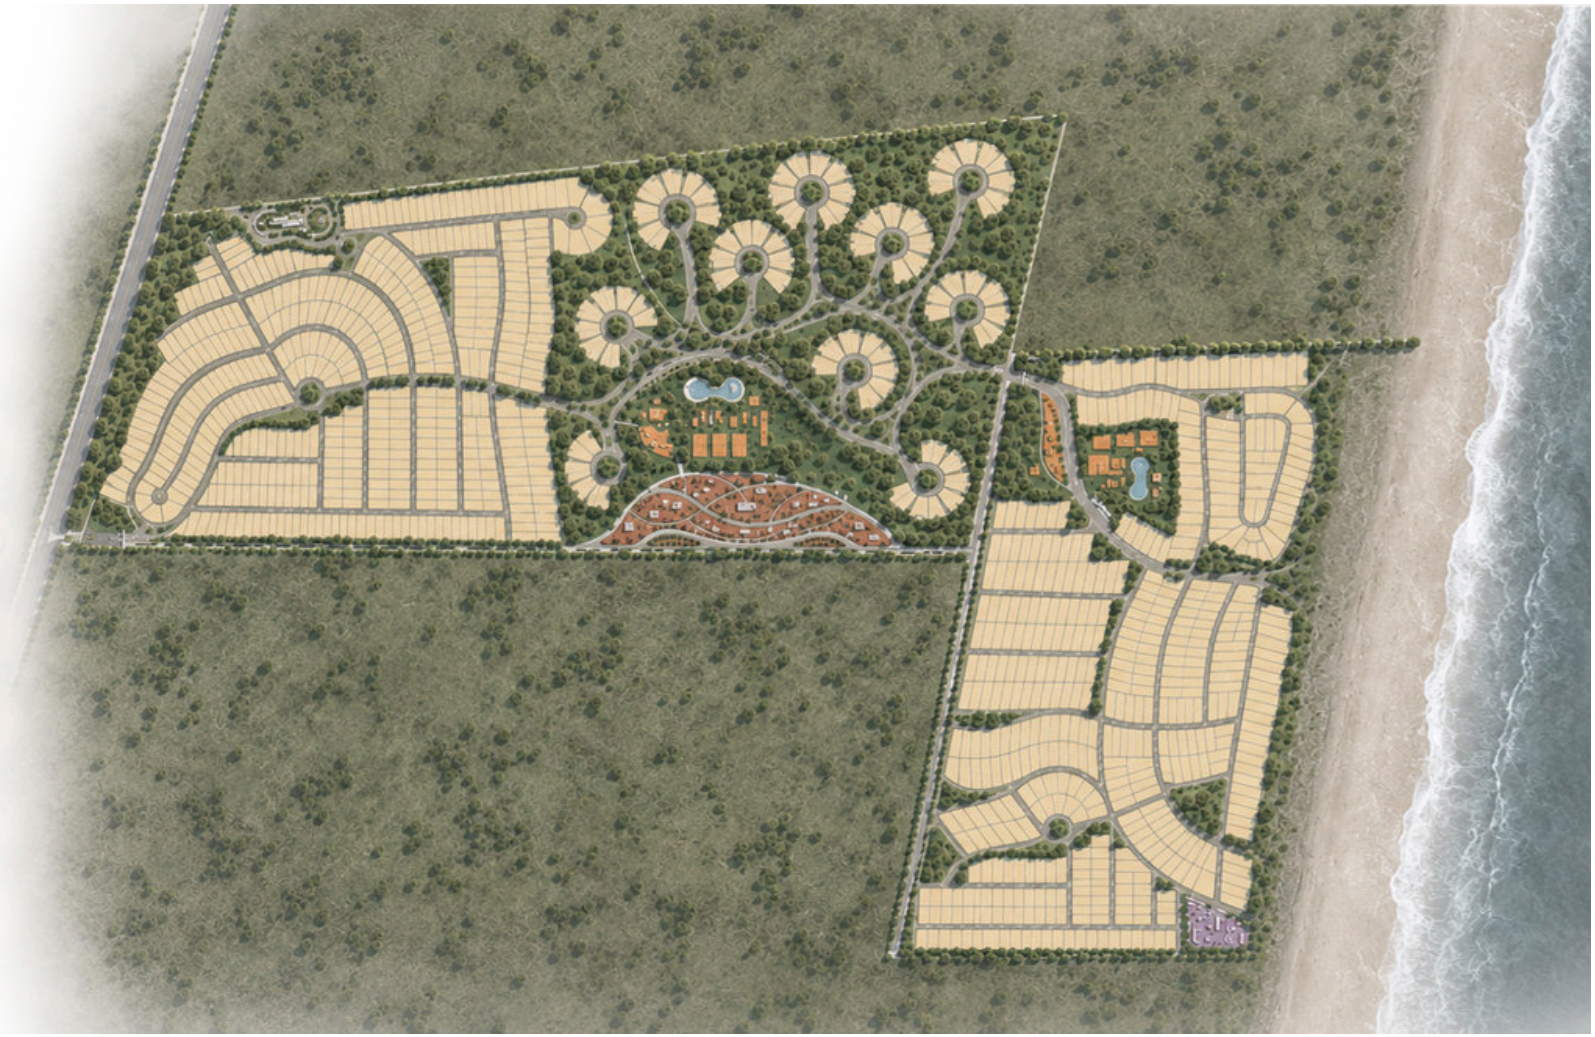

BARRIO I



Barrio residencial de mayor densidad conectado al acceso principal del desarrollo. Integrado con espacios verdes y la topografía natural del entorno.

- Circuito ecuestre



BARRIO II



Sector central con lotes de mayor superficie destinado a actividades deportivas, recreativas y gastronómicas. Incluye el paseo comercial de uso semi público integrado al bosque.

- Deportes
- Gastronomía
- Comercial



BARRIO III



Barrio costero de baja densidad con lotes frente al mar, acceso directo a la playa, beach club y sector destinado a alquileres temporarios.

- Deportes
- Recreación



PROYECTO

08

DOCUMENTACION EJECUTIVA

Documentación técnica para edificios residenciales en altura, desarrollada durante todas las etapas del proyecto ejecutivo.

ROL

Documentación Técnica

CLIENTE

SYGSA


AÑO

2022 - 2024

SOFTWARE

AutoCAD


SketchUp

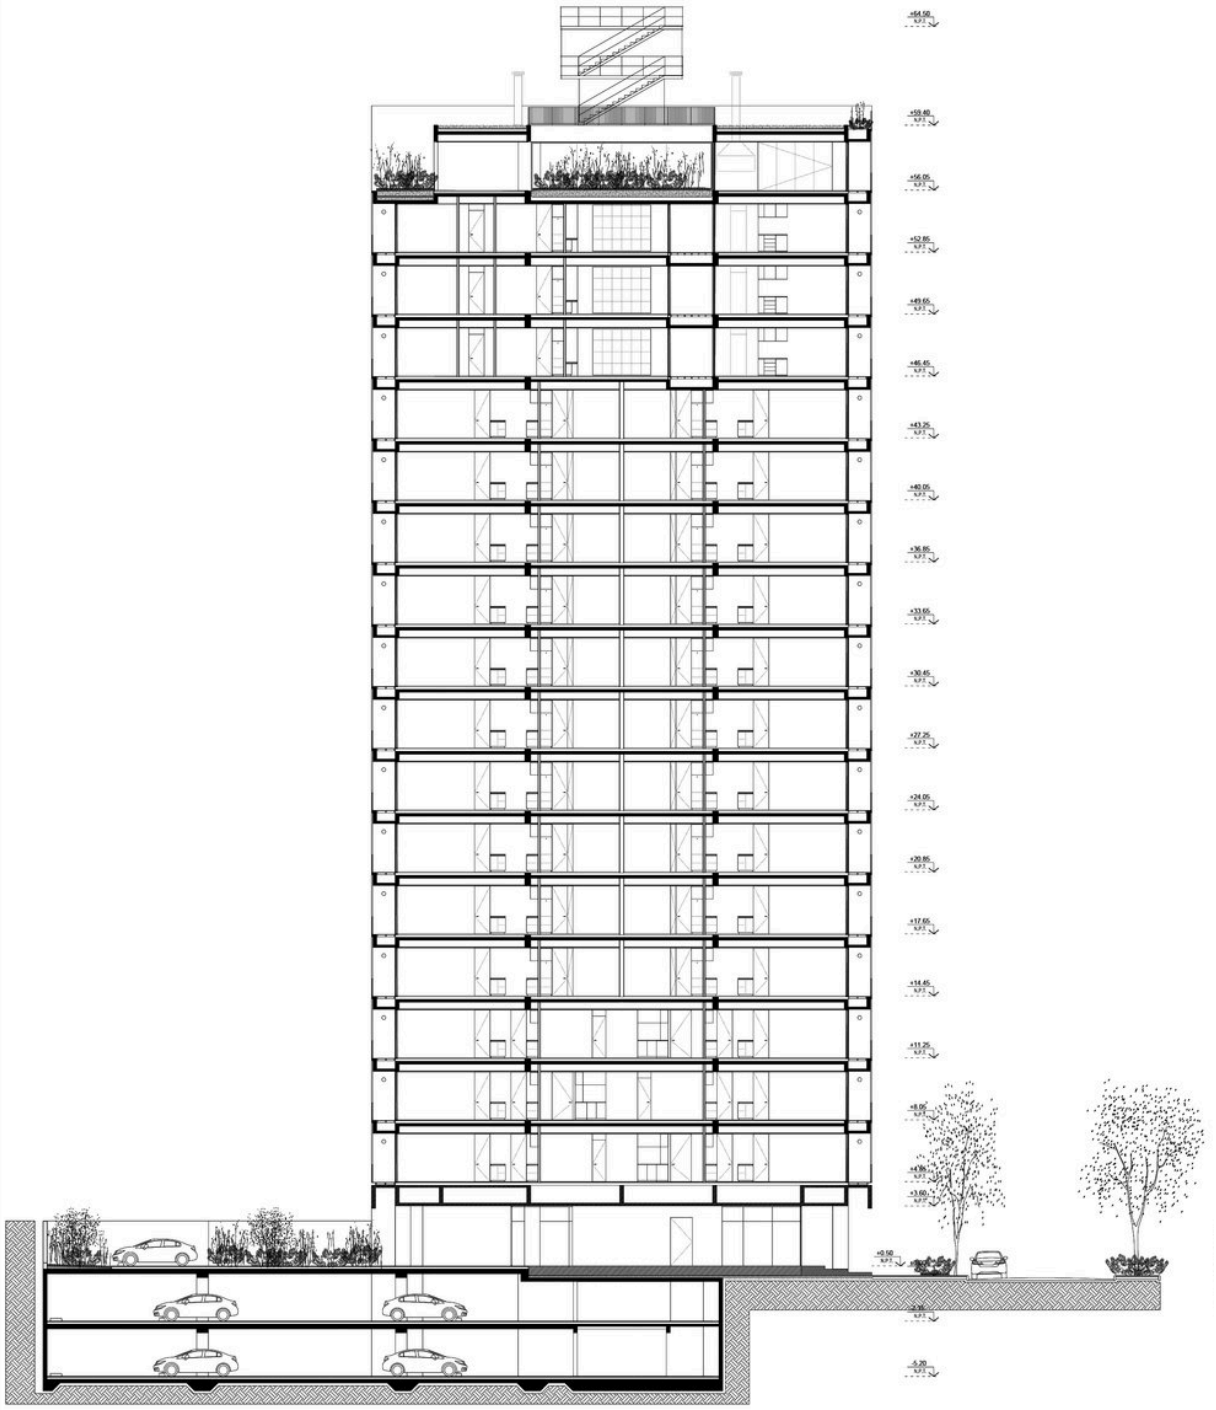


CORTE



PLANTA 7MO PARCIAL (CONTRAFRENTE) - ESCALA 1:50

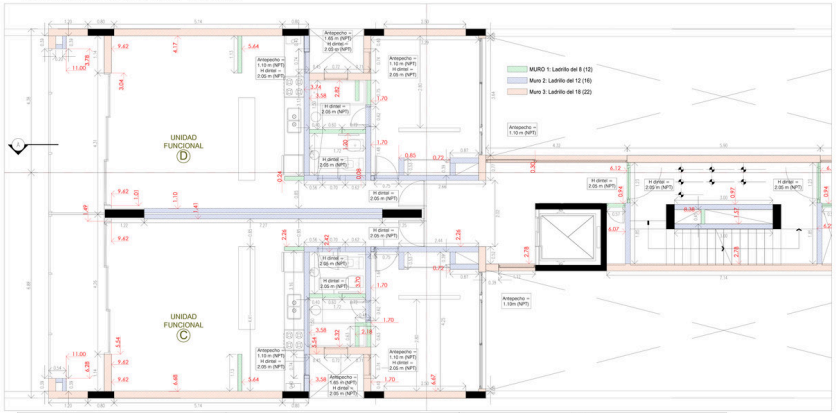

PLANTA PARCIAL - ESCALA 1:1500

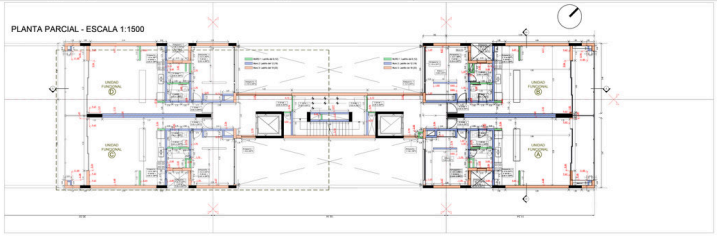


PLANILLA DE MUEBLES

UBICACION - PLANTA TIPO - COCINA

CANTIDAD: 36 de c/u

OBRA: 15.38.39

M 01/M 02/M 03

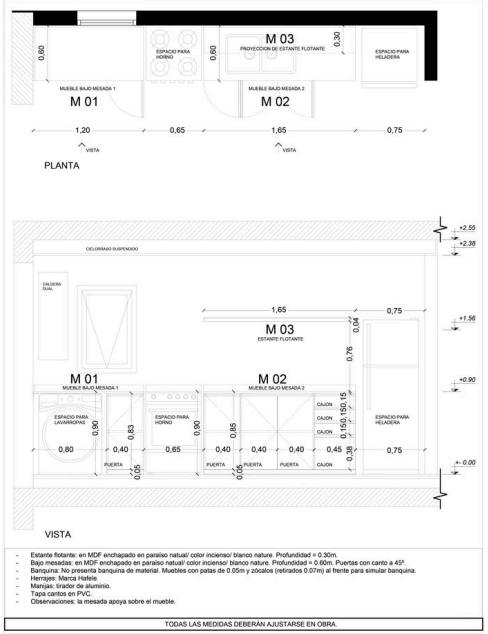


- Estante flotante: en MDF enchapado en paraiso natual/ color incienso/ blanco nature. Profundidad = 0.30m.
- Bajo mesadas: en MDF enchapado en paraiso natual/ color incienso/ blanco nature. Profundidad = 0.60m. Puertas con canto a 45º.
- Banquina: No presenta banquina de material. Muebles con patas de 0.05m y zócalos (retirados 0.07m) al frente para simular banquina.
- Herrajes: Marca Hafele.
- Manijas: tirador de aluminio.
- Tapa cantos en PVC.
- Observaciones: la mesada apoya sobre el mueble.

TODAS LAS MEDIDAS DEBERÁN AJUSTARSE EN OBRA.

DETALLE DE ELECTRICIDAD EN COCINA

UBICACION - PLANTA TIPO - COCINA

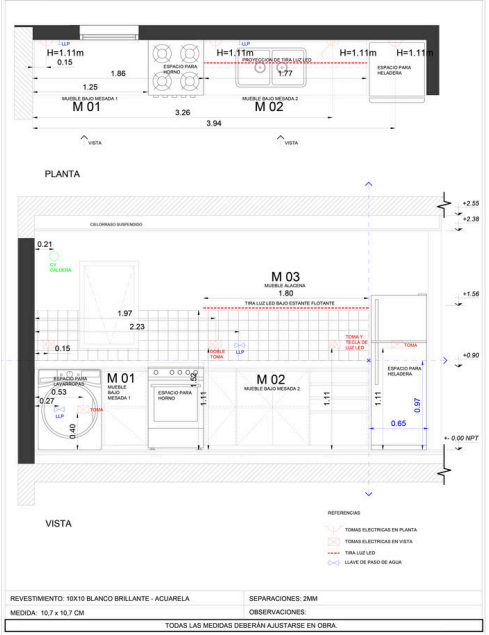

REVESTIMIENTO: 10X10 BLANCO BRILLANTE - ACUARELA

MEDIDA: 10,7 x 10,7 CM

SEPARACIONES: 2MM

OBSERVACIONES:

TODAS LAS MEDIDAS DEBERÁN AJUSTARSE EN OBRA.

PLANILLA DE PARASOLES

UBICACION - BALCON


CANTIDAD: 36


Esc. 1:25


Planta Tipo

FORMA DE ABRIR:	PAÑOS CORREDIZOS Y APILABLES - SISTEMA DE RIELES	MATERIALIDAD:	ALUMINIO
MALLA:	METALICA A DEFINIR	COLOR:	A COTIZAR EN GRIS Y ANODIZADO NATURAL


TODAS LAS MEDIDAS SERAN VERIFICADAS EN OBRA

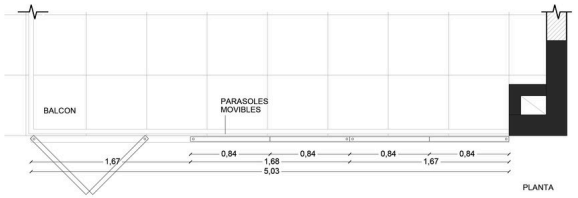

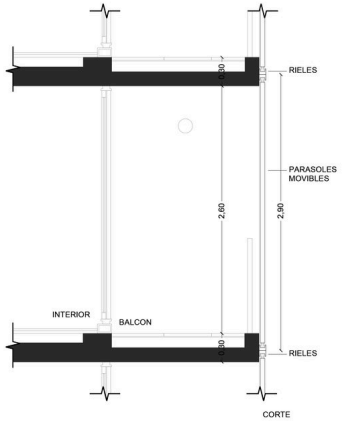

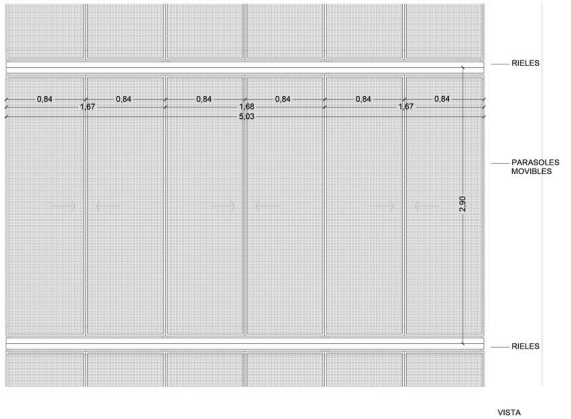


REPLANTEO DE MUROS

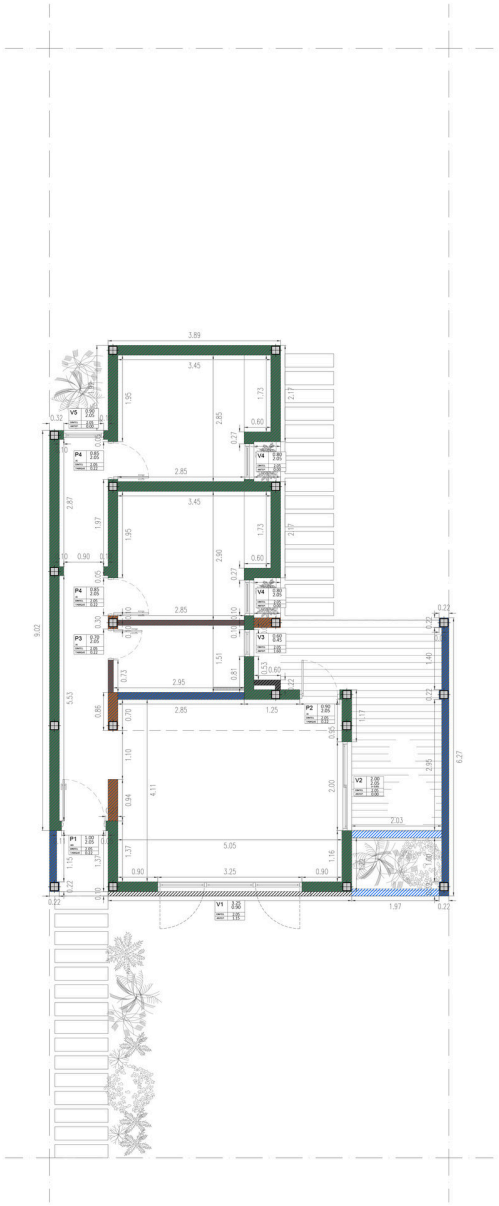

REFERENCIAS


- Tabique de hormigón
- Muro 1: Mixto ladrillo del 12 + subestructura de woodframe
- Muro 2: Ladrillo del 18
- Muro 3: Ladrillo del 12
- Muro 4: Placa de Yeso Doble
- Muro 5: Placa de Yeso Simple

M1 EXTERIOR

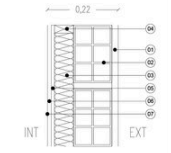


01 - REVOQUE GRUESO + REVOQUE FINO + PINTURA LATEX EXT. 3 MANOS
02 - LADRILLO HUECO CERAMICO ESP. 12CM
03 - AISLACIÓN TERMICA / LANA DE VIDRIO DE 5CM
04 - SOLERA + MONTANTE DE MADERA PINO O EUCALIPTO
05 - BARRERA DE VAPOR
06 - PLACA DE YESO MASILLADA Y PINTADA

M2 EXTERIOR

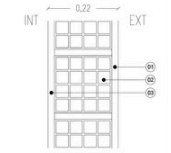


01 - REVOQUE GRUESO + REVOQUE FINO + PINTURA LATEX EXT. 3 MANOS
02 - LADRILLO HUECO CERAMICO ESP. 18CM
03 - REVOQUE GRUESO + REVOQUE FINO + ENDUIDO AL YESO + PINTURA LATEX INT. 3 MANOS

M3 EXTERIOR

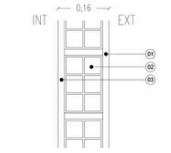

01 - REVOQUE GRUESO + REVOQUE FINO + PINTURA LATEX EXT. 3 MANOS
02 - LADRILLO HUECO CERAMICO ESP. 12CM
03 - REVOQUE GRUESO + REVOQUE FINO + ENDUIDO AL YESO + PINTURA LATEX INT. 3 MANOS

M4 INTERIOR
M5 (IGUAL SIN 1 PLACA)

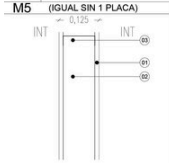

01 - PLACA DURLOCK RESISTENTE A LA HUMEDAD DE 12,5MM
02 - PERFILES MONTANTE: 35MMX90MMX30MM, CON PERFORACIONES PARA PASAJE DE INSTALACIONES.
03 - PERFILES SOLERA: 35MMX100MMX29MM


PROVISION AGUA FRIA Y CALIENTE







ELECTRICIDAD (TOMAS)




ELECTRICIDAD (LUCES)

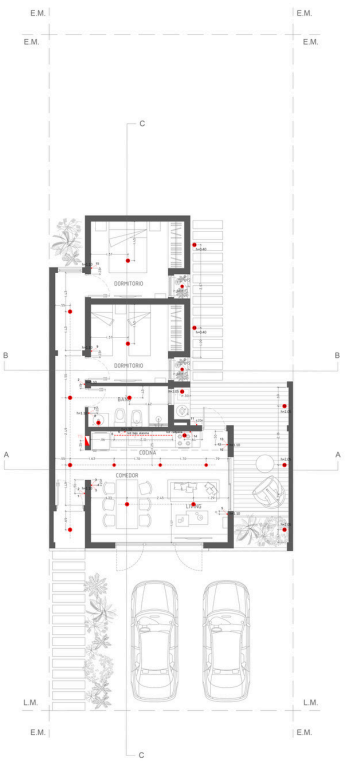

PLANILLA DE CARPINTERIAS

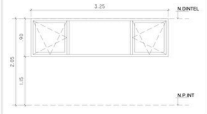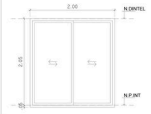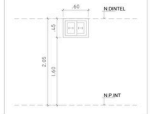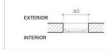DESIGNACIÓN	V1	3.25 0.90	V2	2.00 2.05 (+ 0.05)	V3	0.60 0.45
	DINTEL	2.05	DINTEL	2.05	DINTEL	2.05
	ANTEPECHO	1.15	ANTEPECHO	0.00	ANTEPECHO	1.60
DESTINO	Cocina		Living		Baño	
CANTIDAD	1		1		1	
VISTA Esc.1:100						
PLANTA						
NOTAS	- Las carpinterias están dibujadas vistas desde el interior. - Todas las carpinterias llevan premarco. - Todas las carpinterias llevan mochetas de mínimo 5 cm para colocación de contramarcos.		- Las carpinterias están dibujadas vistas desde el interior. - Todas las carpinterias llevan premarco. - Todas las carpinterias llevan mochetas de mínimo 5 cm para colocación de contramarcos.		- Las carpinterias están dibujadas vistas desde el interior. - Todas las carpinterias llevan premarco. - Todas las carpinterias llevan mochetas de mínimo 5 cm para colocación de contramarcos.	
LÍNEA	MODENA		MODENA		MODENA	
APERTURA	2 OSCILOBATIENTES + PAÑO FIJO		CORREDIZA		CORREDIZA	
HOJA	3 HOJAS		2 HOJAS		2 HOJAS	
PAÑO	VIDRIO		VIDRIO		VIDRIO	
MATERIAL	ALUMINIO		ALUMINIO		ALUMINIO	
MARCO	ALUMINIO		ALUMINIO		ALUMINIO	
VIDRIO	DVH		DVH		DVH	
COLOR	BLANCO		BLANCO		BLANCO	

PLANILLA DE MUEBLES

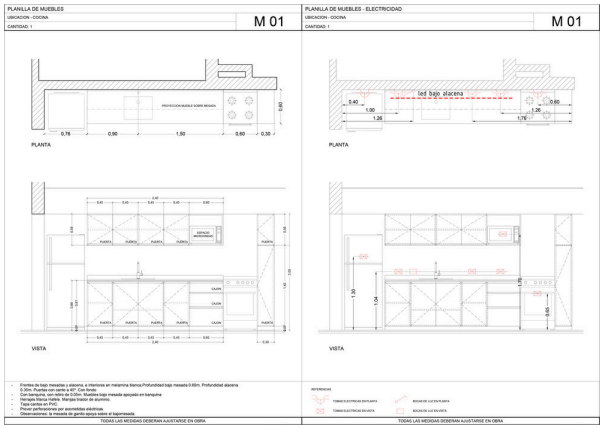



Acompaño todas las etapas del proceso arquitectónico, desde la idea inicial hasta la documentación técnica y la comunicación visual del proyecto.

CONTACTO
halbergmagdalena@gmail.com
+54 9 291 4360696
Monte Grande, Buenos Aires, Argentina